



AI Glasses V2 Phase 1.5 Floorplan Render - placement envelopes in mm


Overall allocation - current schematic driven placement concept

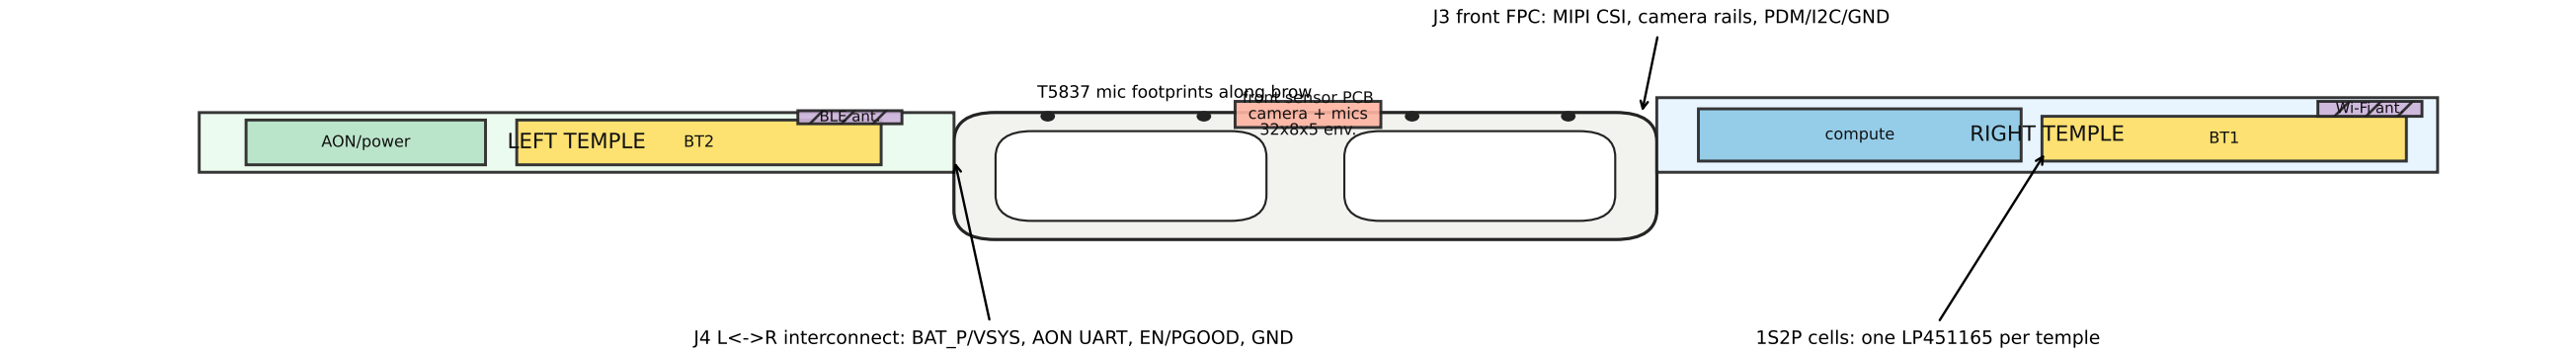

Right temple top view - compute + Wi-Fi + battery

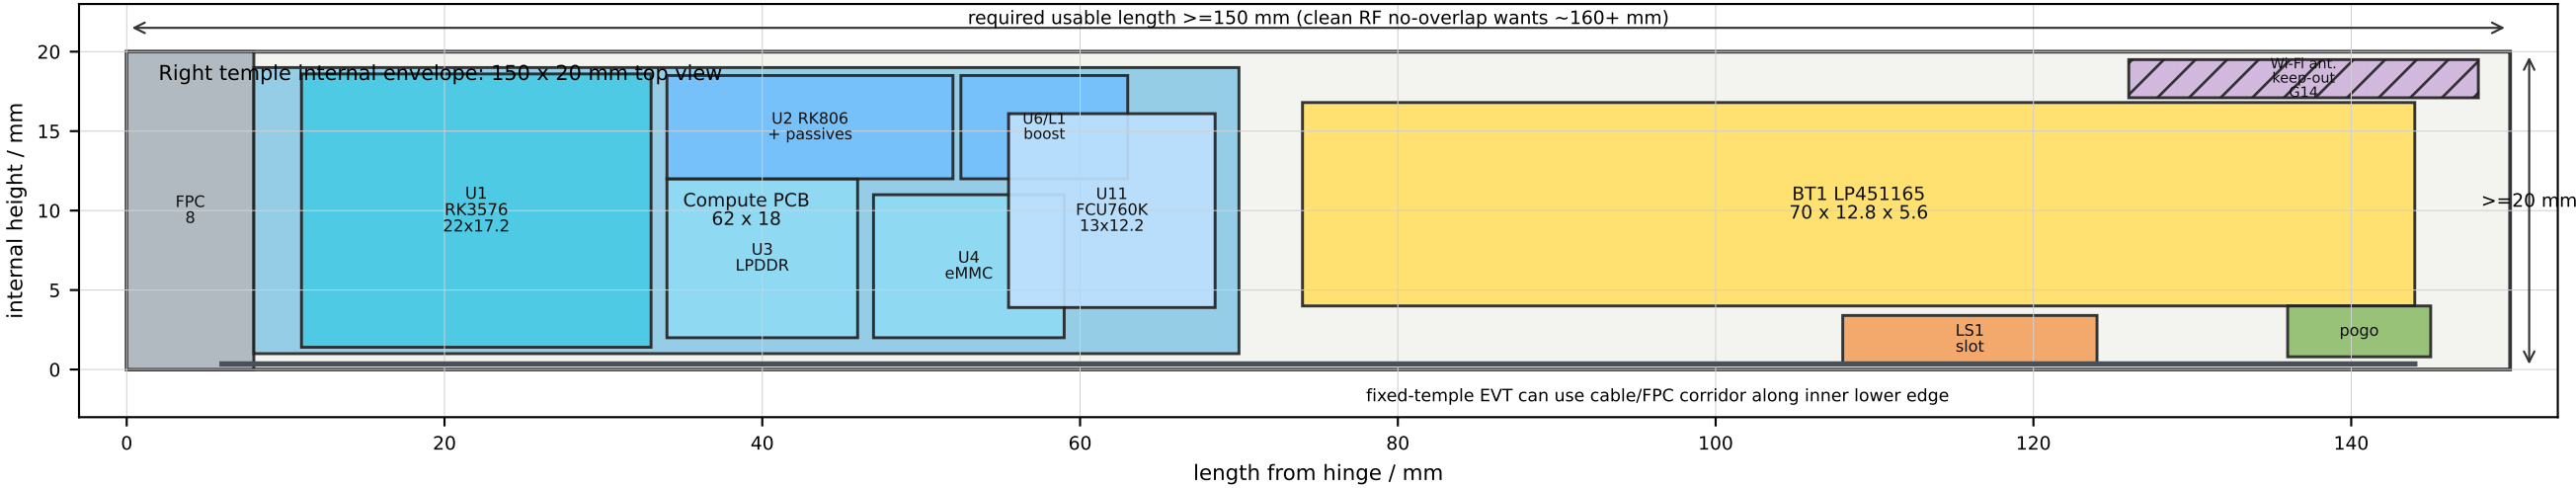

Left temple top view - AON/power + battery

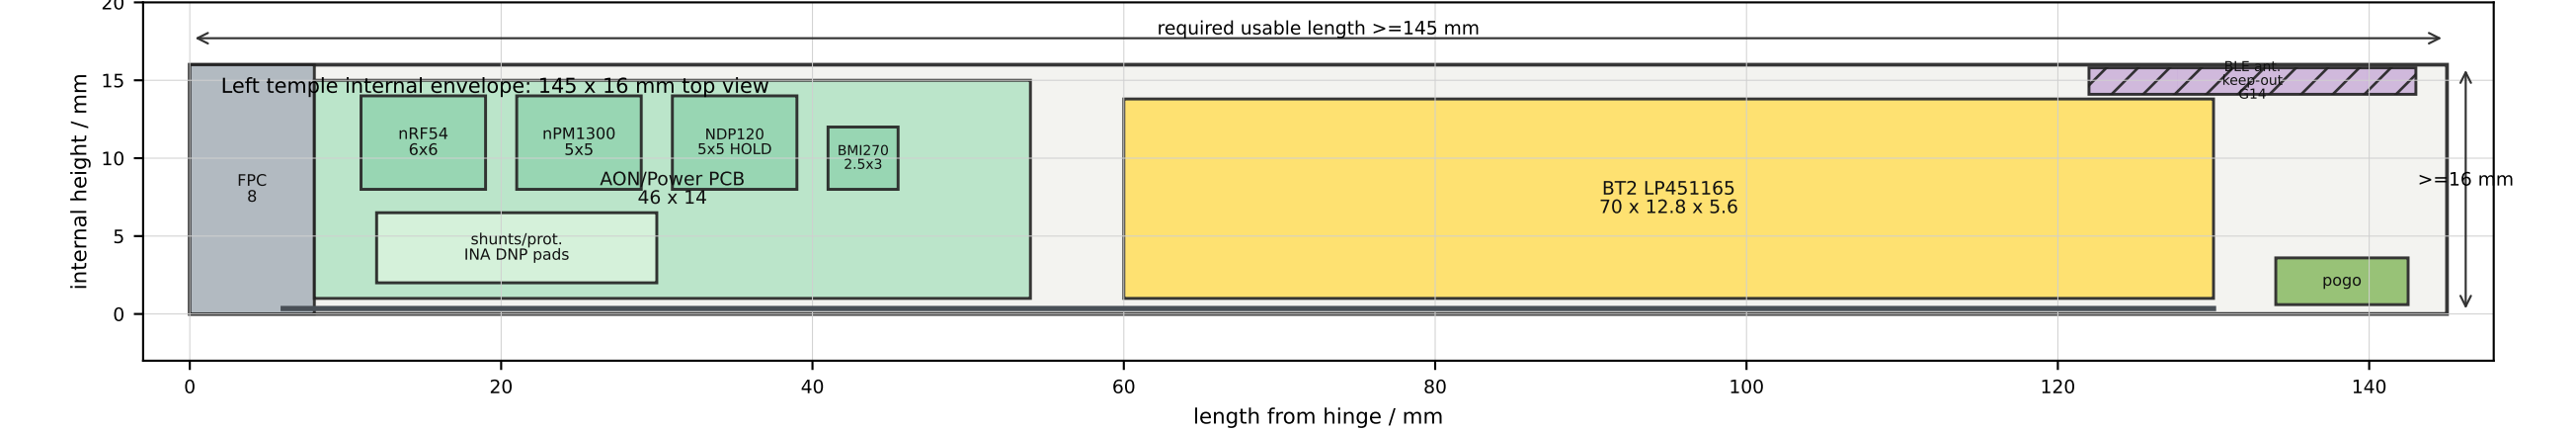

Right side section - thickness stack, no battery under RK3576

